


PREFABRICATED HOUSING COMPLEX

FROM AS-BUILT SURVEY TO PARAMETRIC BIM

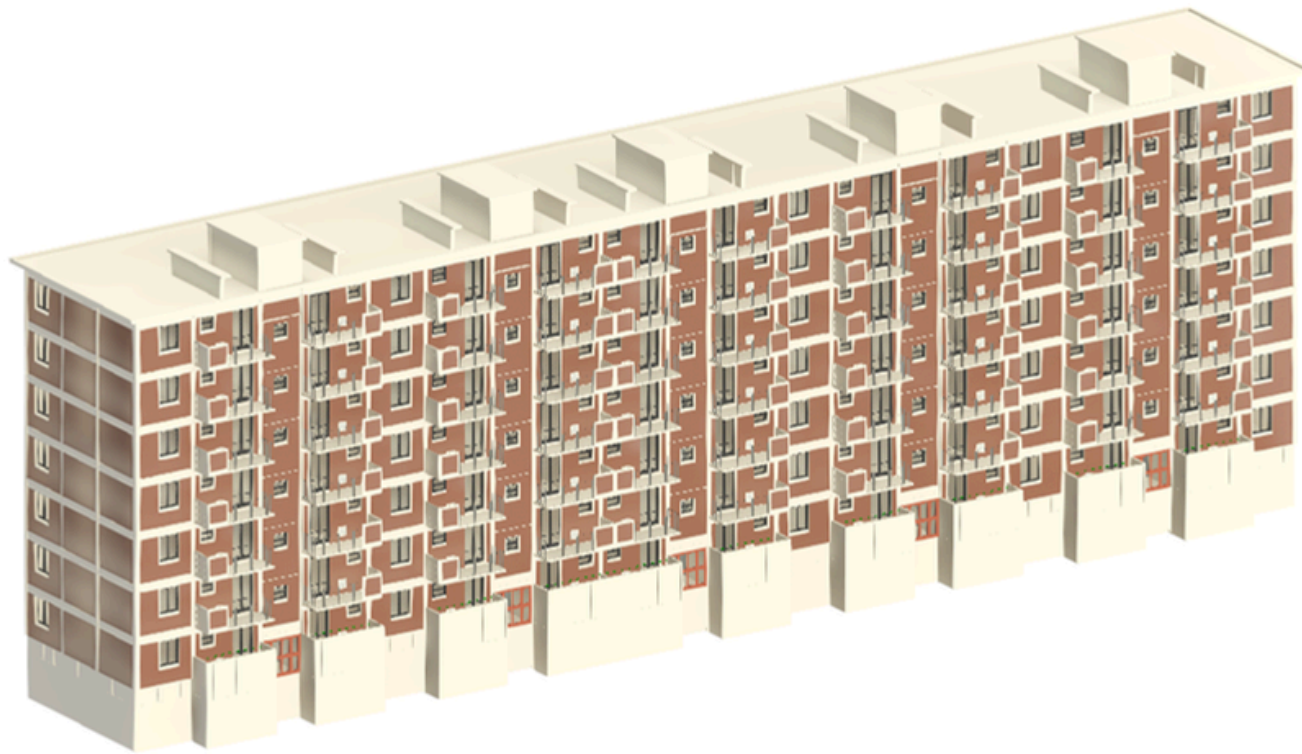

TYPE: BIM


YEAR: 2024

TEAM: Andrea Cutroni &
Alessandro Abagnale

FACULTY: Ilaria Giannetti

CONTEXT: Academic course
“Digital processes for building
design and construction”


The project involves the development of a BIM model in Revit of an existing prefabricated housing complex built in the 1960s and situated near Milan. The modelling process is based on historical documentation, original patents and as-built conditions surveyed via Google Maps. It includes both architectural and structural modeling, with personalized parametric families, alongside the creation of a Common Data Environment and the extraction of data into Excel files.

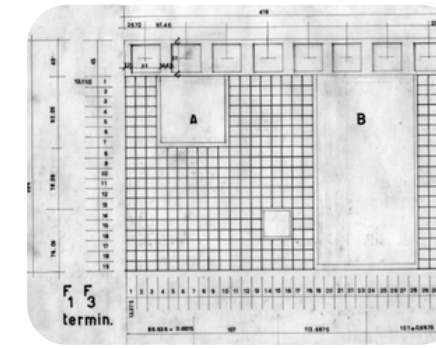


FACADE PANEL CATALOGUING

Legenda


- Pff-04A x7
- PFb-01A x30
- PFb-02A x5
- Pff-05 x5
- Pff-06 x25
- PFc-04 x5
- PFb-01B x30
- PFb-02B x5
- Pff-02B x7
- Pff-02A x14
- Pff-04B x7

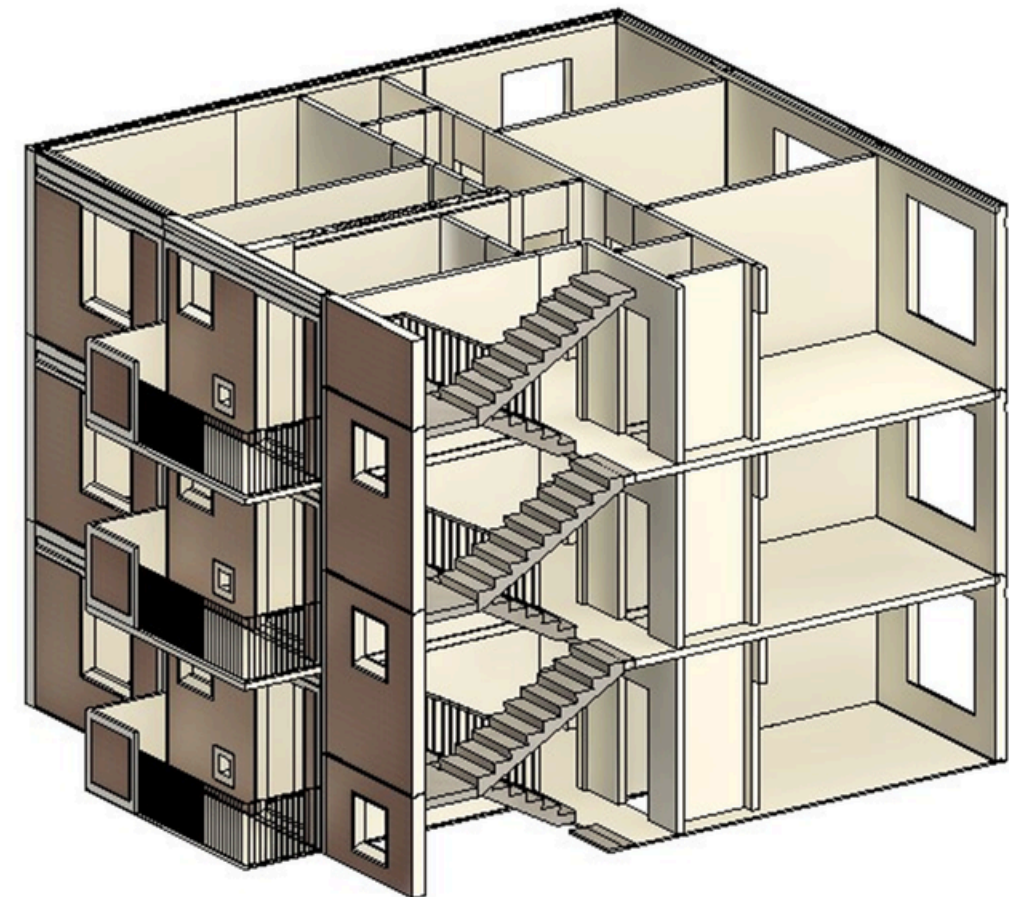

ARCHITECTURAL MODELING

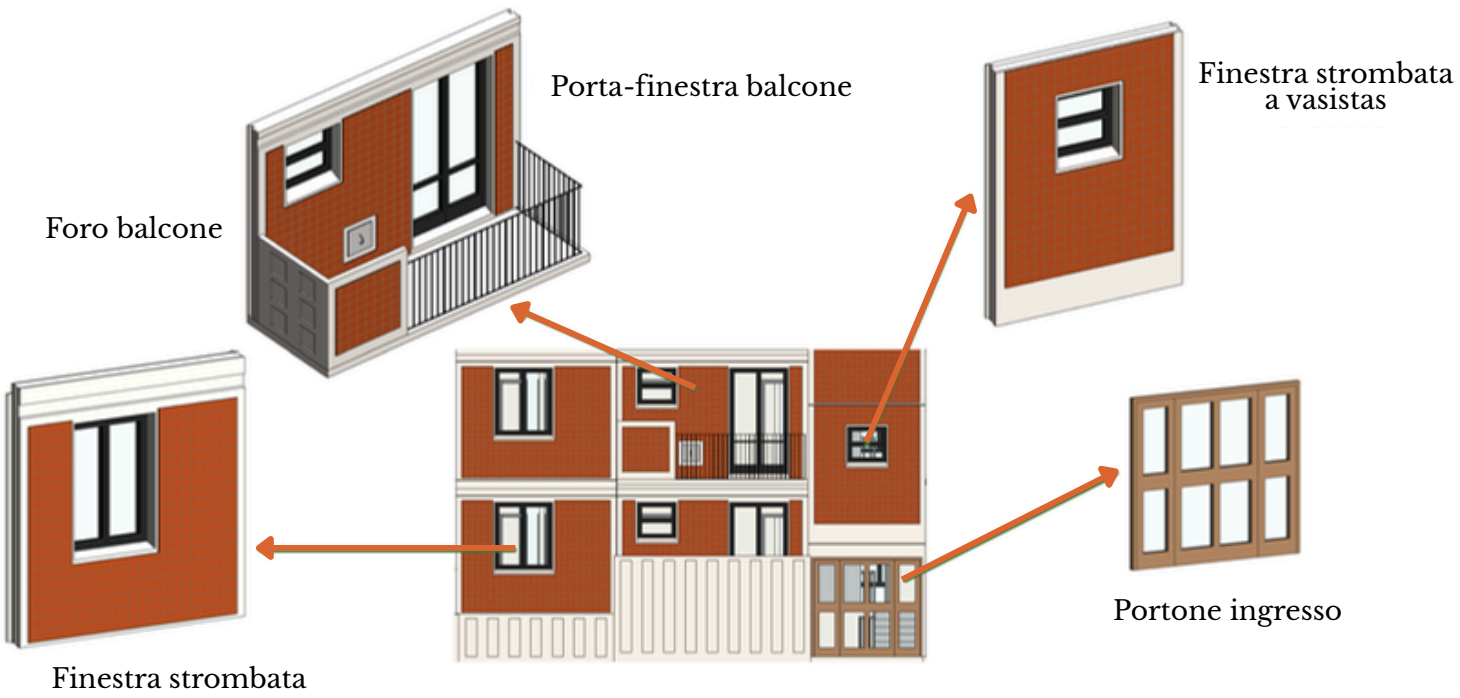

STRUCTURAL MODELING

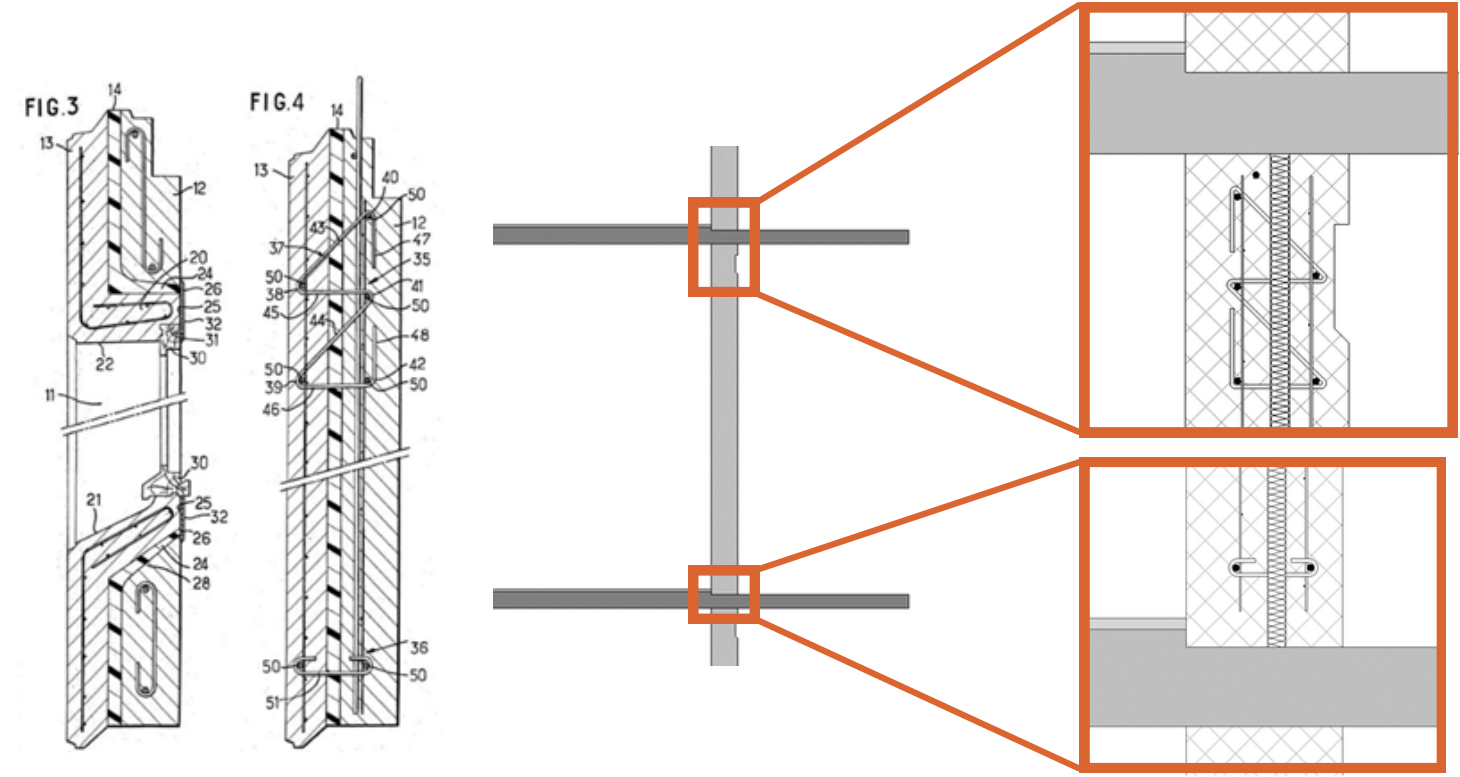


Pfb-01A
Pannello di facciata con finestra tipo 04A

Dimensioni
4,26 x 2,87 m x 0,22 m

Posizione
Prospetto Sud

- Componenti**
1. Pannello prefabbricato in c.a. con strato isolante, porta finestra e finestra strombata
 2. Rivestimento in klinker
 3. Fogli di rete metallica
 4. Barre di armatura
 5. Sollevatori

Strutturale	
Copri ferro armatura - Su...	Rete esterna-MBM <50 ...
Copri ferro armatura - Su...	Rete interna-MBM <75 ...
Copri ferro armatura - Al...	XA2 -XC4 <25 mm>
Volume armatura stimato	2228.57 cm ³
Quote	
Volume	1.805 m ³
Area	8.204 m ²
Lunghezza	425.50
Altezza	286.50
Spessore	22.00
Esclusione	☐
La forma è stata modificata...	
Deti identità	
Nome assieme	Pfb-01A-5-02-02
Immagine	
Commenti	
Contrassegno	Pfb-01A
Mostra punti di manipol...	☐
Categoria originale	Muri
Famiglia originale	Muro di base
Tipo originale	MBM-PF-220 mm

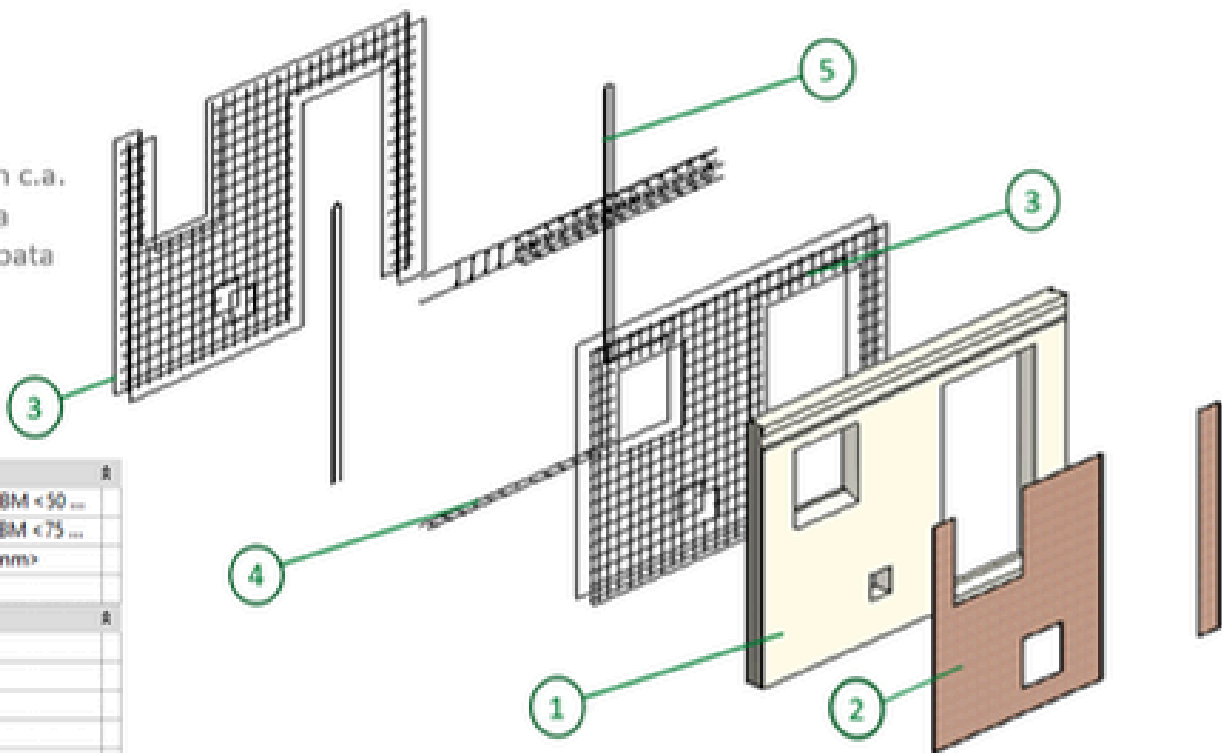

Deti identità	
Immagine tipo	
Nota chiave	
Modello	
Prodotto da	
Commenti sul tipo	Pannello di facciata con balcone tipo 01A
URL	https://drive.google.com/file/d/1UkT1w2j8M4c5Cem8Iwem739Ivteashd/view?usp=sharing
Descrizione	Pannello prefabbricato autoportante realizzato con stampi di dimensioni variabili
Descrizione assieme	
Codice assieme	
Contrassegno tipo	Pfb-01A
Corte	

